PORTFOLIO

GIULIA LONGHI

5409 S.Blackstone Ave.
+1 312 792 1227
gllonghi@yahoo.it
giulialonghi.com

GIULIA LONGHI
ARCHITECT

5409 S.Blackstone Ave
60615 Chicago - IL
+1 312 792 1227
gllonghi@yahoo.it
giulialonghi.com

SOFTWARE

Microsoft Office_
ILLUSTRATOR cc
PHOTOSHOP cc
INDESIGN cs6
LIGHTROOM cc
MUSE cc

AUTOCAD 2014
VECTORWORKS2015
ARTLANTISstudio
3D STUDIO
SKETCH UP pro

EDUCATION

2014 **Master's "Intelligent School Design"**

2014 **Italian Qualifying Examination** - licensed to practice as architect in Italy and throughout the European Union

2013 **Master's degree in Architecture for sustainability at IUAV** (Rated in the top 5 architecture universities in Italy)

2010 **Bachelor's degree in Architecture at IUAV** - Istituto Universitario di Architettura di Venezia

2009 **FSE Professionalizing Course for Expert in digital modeling for architecture and landscape**

2007 **Artistic high school degree LAS** Liceo Artistico Statale di Venezia

LANGUAGES

Italian mother tongue
English very good
Japanese base knowledge

PUBLICATIONS

On-going **Il fondaco, archetipo e prototipo per un'architettura mediterranea sostenibile** ed.Aracne, by Roberta Albiero, edited by Giulia Longhi

I nuovi fondaci per dialogare con l'oriente, Giuseppe Longhi, edited by.

Progetti di riqualificazione: micro percorsi della mente; Il generatore di sapere; Contribution to Vod-Value of difference, Umbrella Think Tank, Intelligent school design 2014

System thinking, verso una progettazione collaborativa. Contribution to Vod-Value of difference, Umbrella Think Tank, Intelligent school design 2014

Dall'aula alla nuvola, le forze guida della scuola contemporanea. (english/italian translation) Contribute for Vod-Value of difference, Intelligent school design 2014

Giornale IUAV n. 119, edited for AWR - International Ideas Competition of Architecture 2013
Edited by.

PREVIOUS WORKS

2016
A-Office with TAMassociati
Competition "La buona scuola" innovative schools

2014-16
A-Office
Recently for 15. Biennale Architettura in Venice, Italy
Final and executive project. Work supervisor on site for setting-up japanese pavillion, Jaeeun-Choi|Shigeru Ban, on the 15th International Architecture Exhibition.
Work supervisor on the Italian Pavillion, Tam Associati, curatorial team.

2016
Nova Marghera Co.Ltd
Technical survey and consecutive redraw for the Città della Musica building. Building site in Marghera - Venice interland.

2015
Green communication Co.Ltd
Ecofondaco per Expo Venezia
Collaboration for Graphic and web design realization, pavillion's executive drawings
http://www.venicetoexpo2015.org

2014-2017
Teaching assistent at IUAV - University of architecture in Venice

2014
Randolfi Architects
Photographic and graphic portfolio
Technical surveys and CAD redraw
Image elaboration, rendering
Practice activities, official procedures

2013-2016
Research collaboration
Architectural research, study of archive material in the architecture composition and urban planning for the contemporary cities.
Graphic coordinator and curator at IUAV.
Professors: Roberta Albiero, Giuseppe Longhi

2011
Giovanni Battista Girello Architect
Internship

2006
Studio Seno-Zambon Architects
Summer Internship

MUSEUM

MUSEO DIOCESANO

RENDER, photographic simulation of the interior design

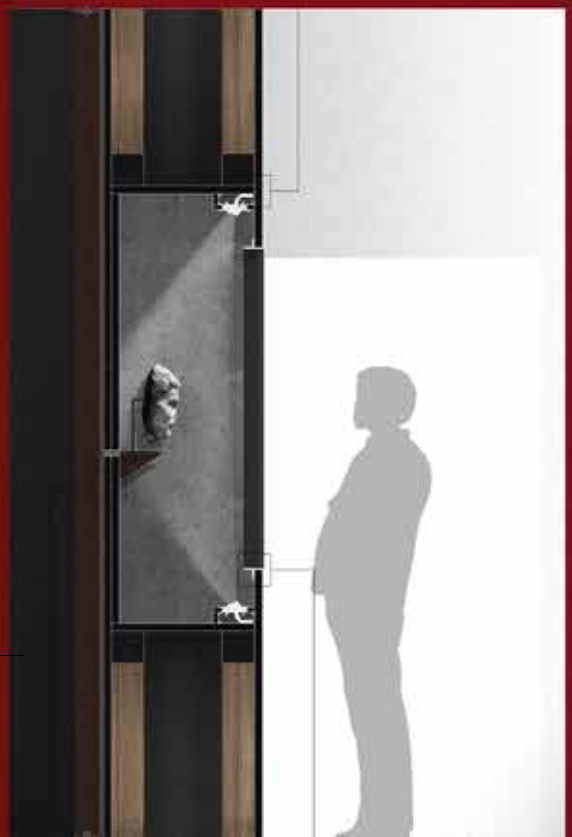

Portico

Exposition rooms

Architectonic details

MUSEUM

MUSEO DIOCESANO

Ground Floor

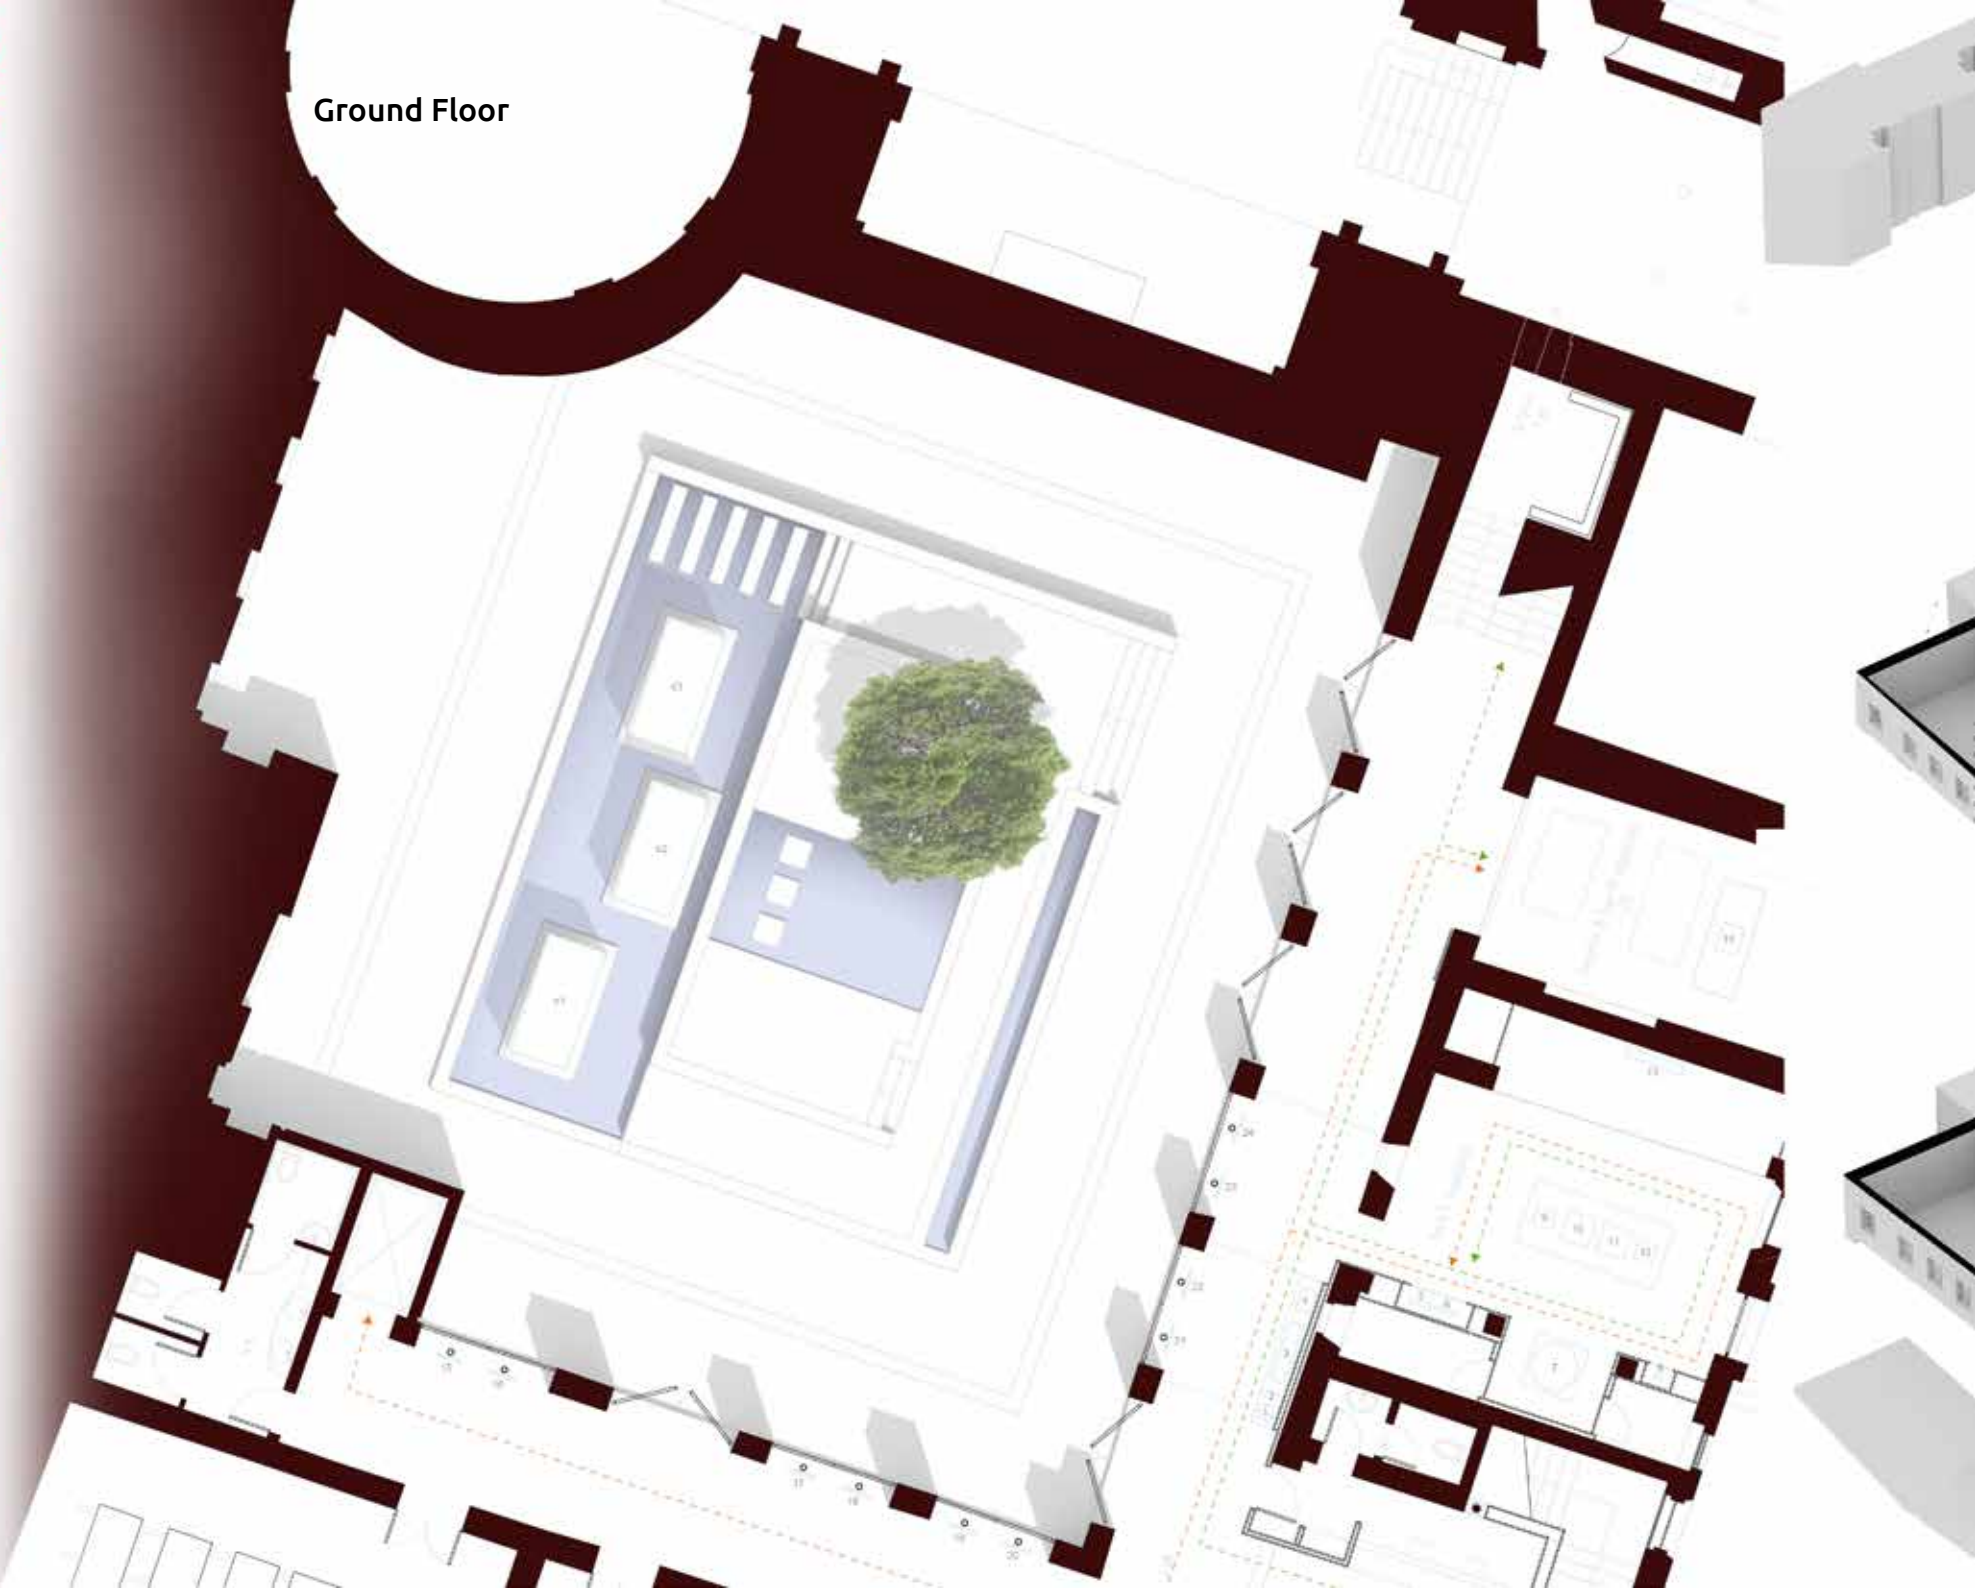

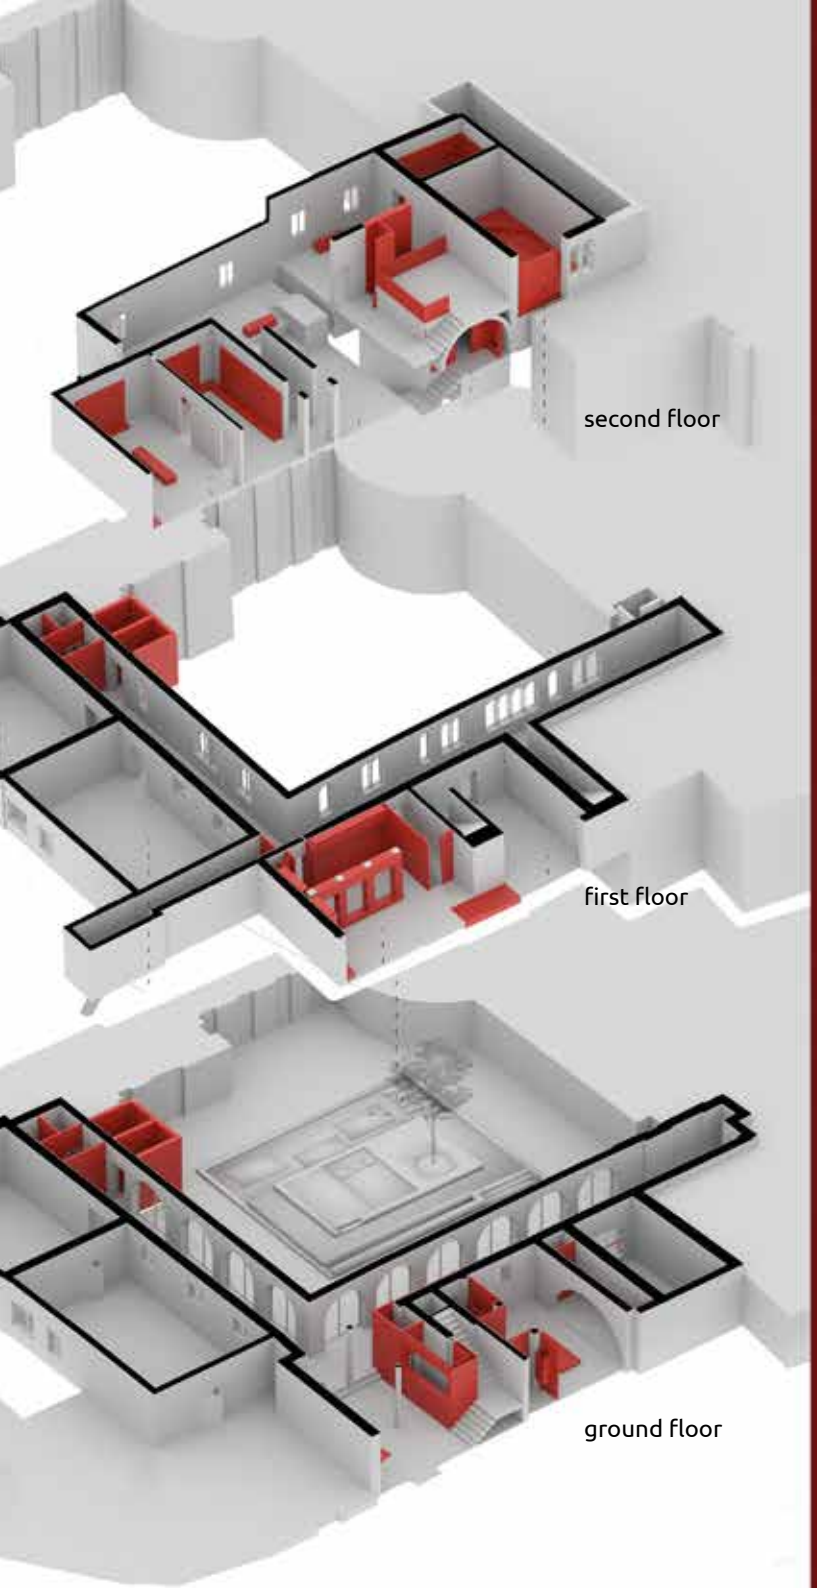

Transverse section

Longitudinal section

MUSEUM

MUSEO DIOCESANO

Axonometric view of the model

Plan of the Exposition room on the ground floor and part of the entrance room.

Section

The Diocesan Museum is situated in the historic center of Treviso city. The building that hosts it is one of the most ancient buildings in the city and is commonly named “Canoniche Vecchie” -old clergy house-, because in the past it hosted the priests of the cathedral. The project entails the restoration of the interior spaces and of the Chiostro and the renovation of the exposition rooms.

LISBOA

HOTEL/SPAZI PUBBLICI

the project entailed the creation of a medium large dimensions hospitality building, including of an area of small houses for temporary stays.
The architectural project was developed considering the surrounding environment that is an abandoned industrial area and the connections with the city of Lisbon.
During the process of designing one of the main concern was the energy efficiency, especially in the summer period.

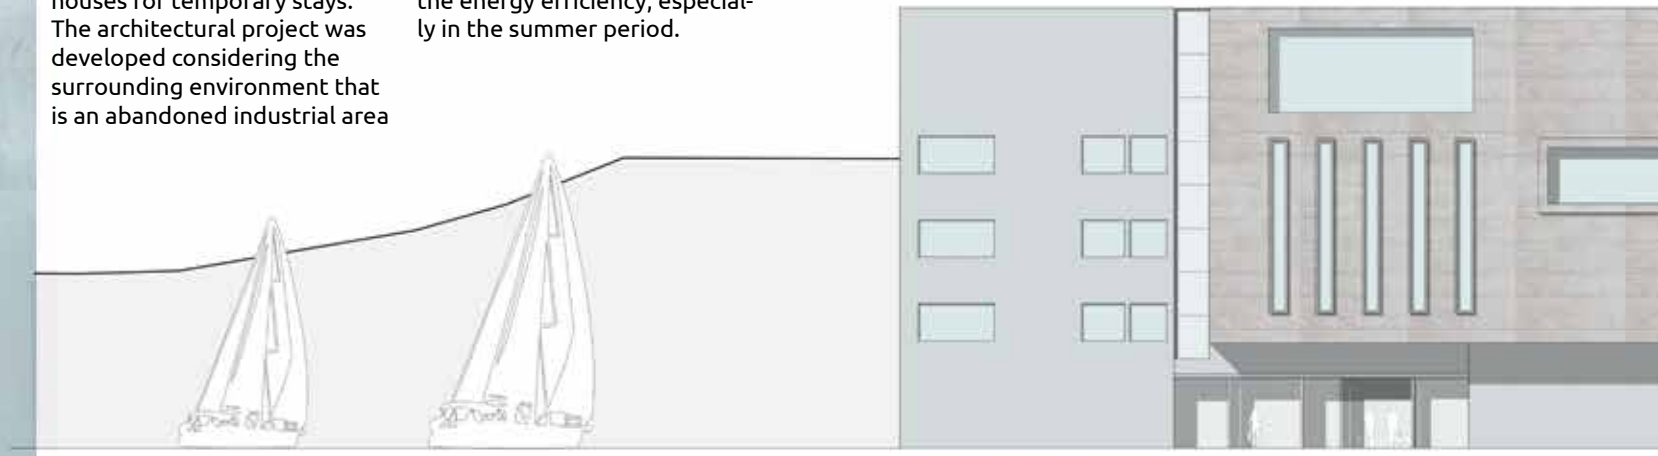

ECOTECT ANALYSIS

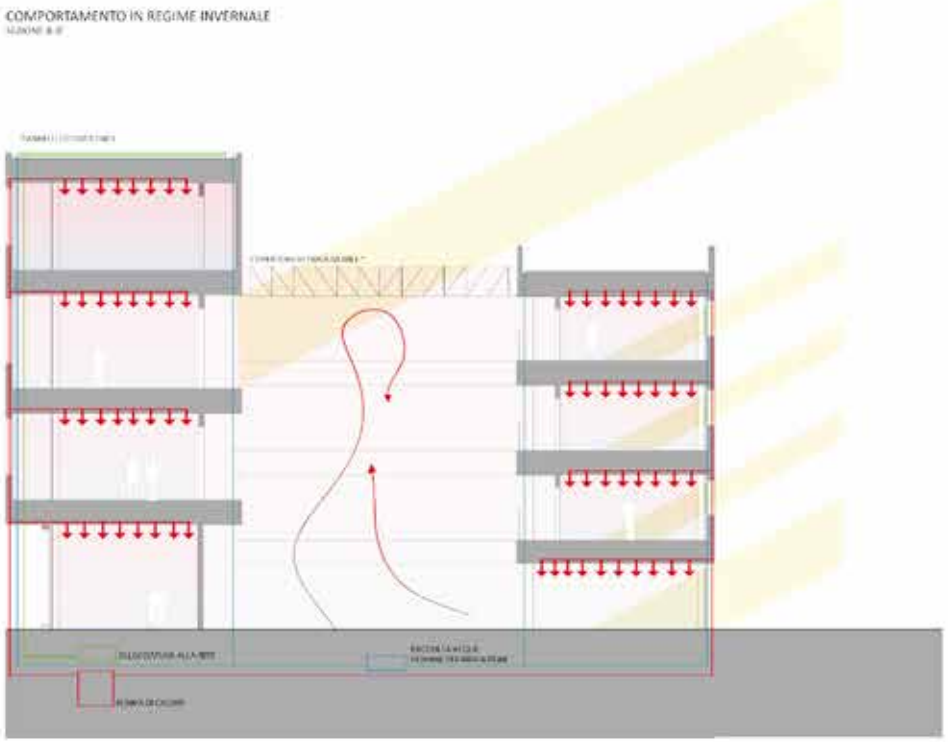

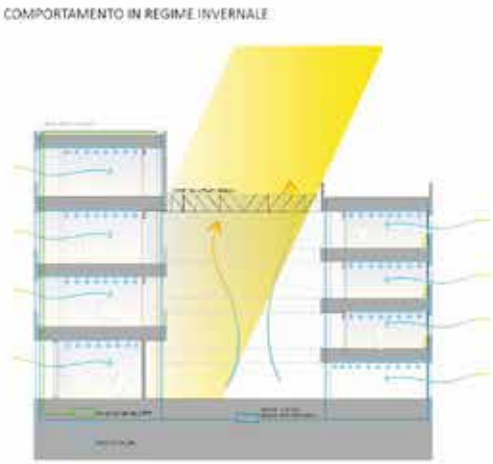

DIAGRAMMI SOLARI

porzione di cielo visibile dal piano terra dell'hotel

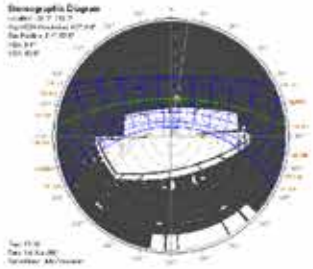

porzione di cielo visibile dal piano primo dell'hotel

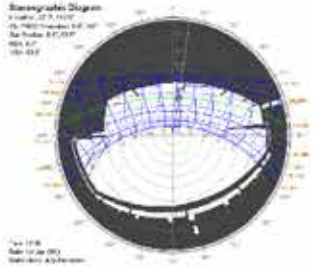

porzione di cielo visibile dal centro dell'area

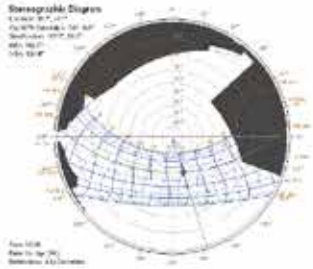

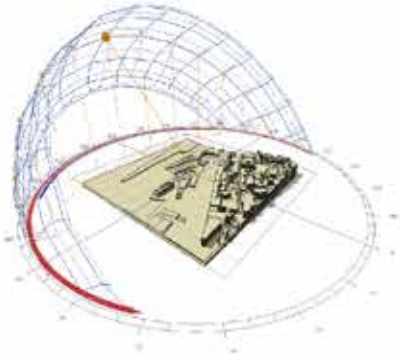

21 DICEMBRE (camera dell'hotel ammobiliata)

21 GIUGNO (camera dell'hotel ammobiliata)

21 DICEMBRE (camera dell'hotel non ammobiliata)

21 GIUGNO (camera dell'hotel non ammobiliata)

LA STANZA

LABORATORIO D'INTERNI

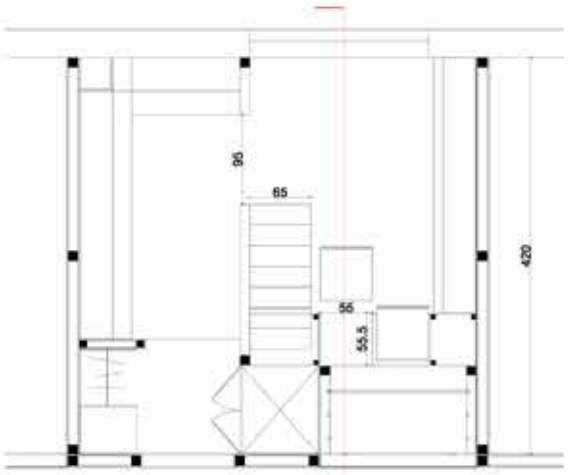

PT

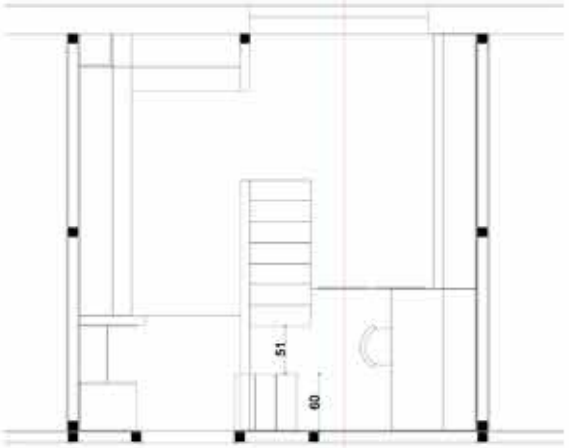

P1

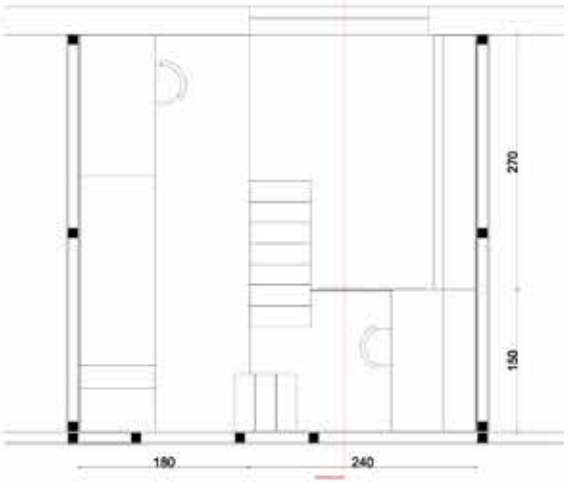

P2

SECTION A-A'

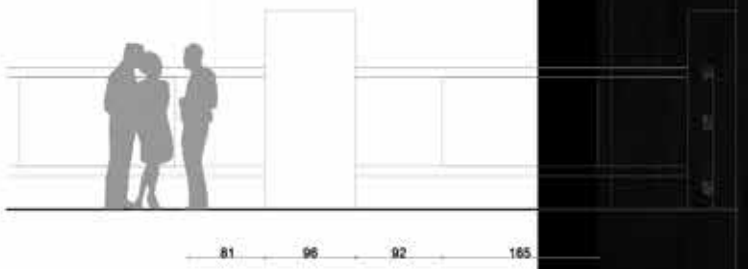

PROSPECT

The project involved the creation of a series of small studios for hosting teachers inside the institute during their stays as professors at IUAV. Those were thought of as temporary capsules to provide new private spaces even in historical buildings.

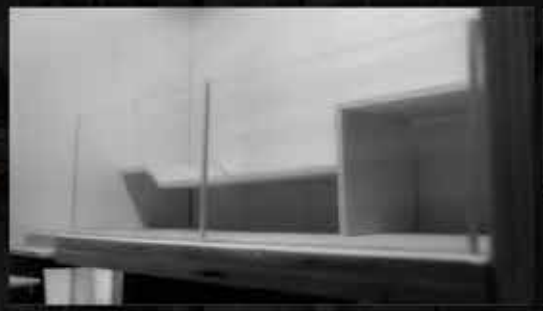

"Architecture comes from the making of a Room"

Louis Kahn

SUBWAY

VENICE_ZATTERE

The sub-lagoon stations can only be decorative elements in the historical city and its lagoon. These, disposing of large lagoonar spaces along the edges of the insular city, are an important occasion for a new architecture in the urban scene, made by pattern, following the same Venitian tradition that has produced small objects based on simple figures. Prototypes able to repeat the same base figure and adapt to different context.

Gianni Fabbri

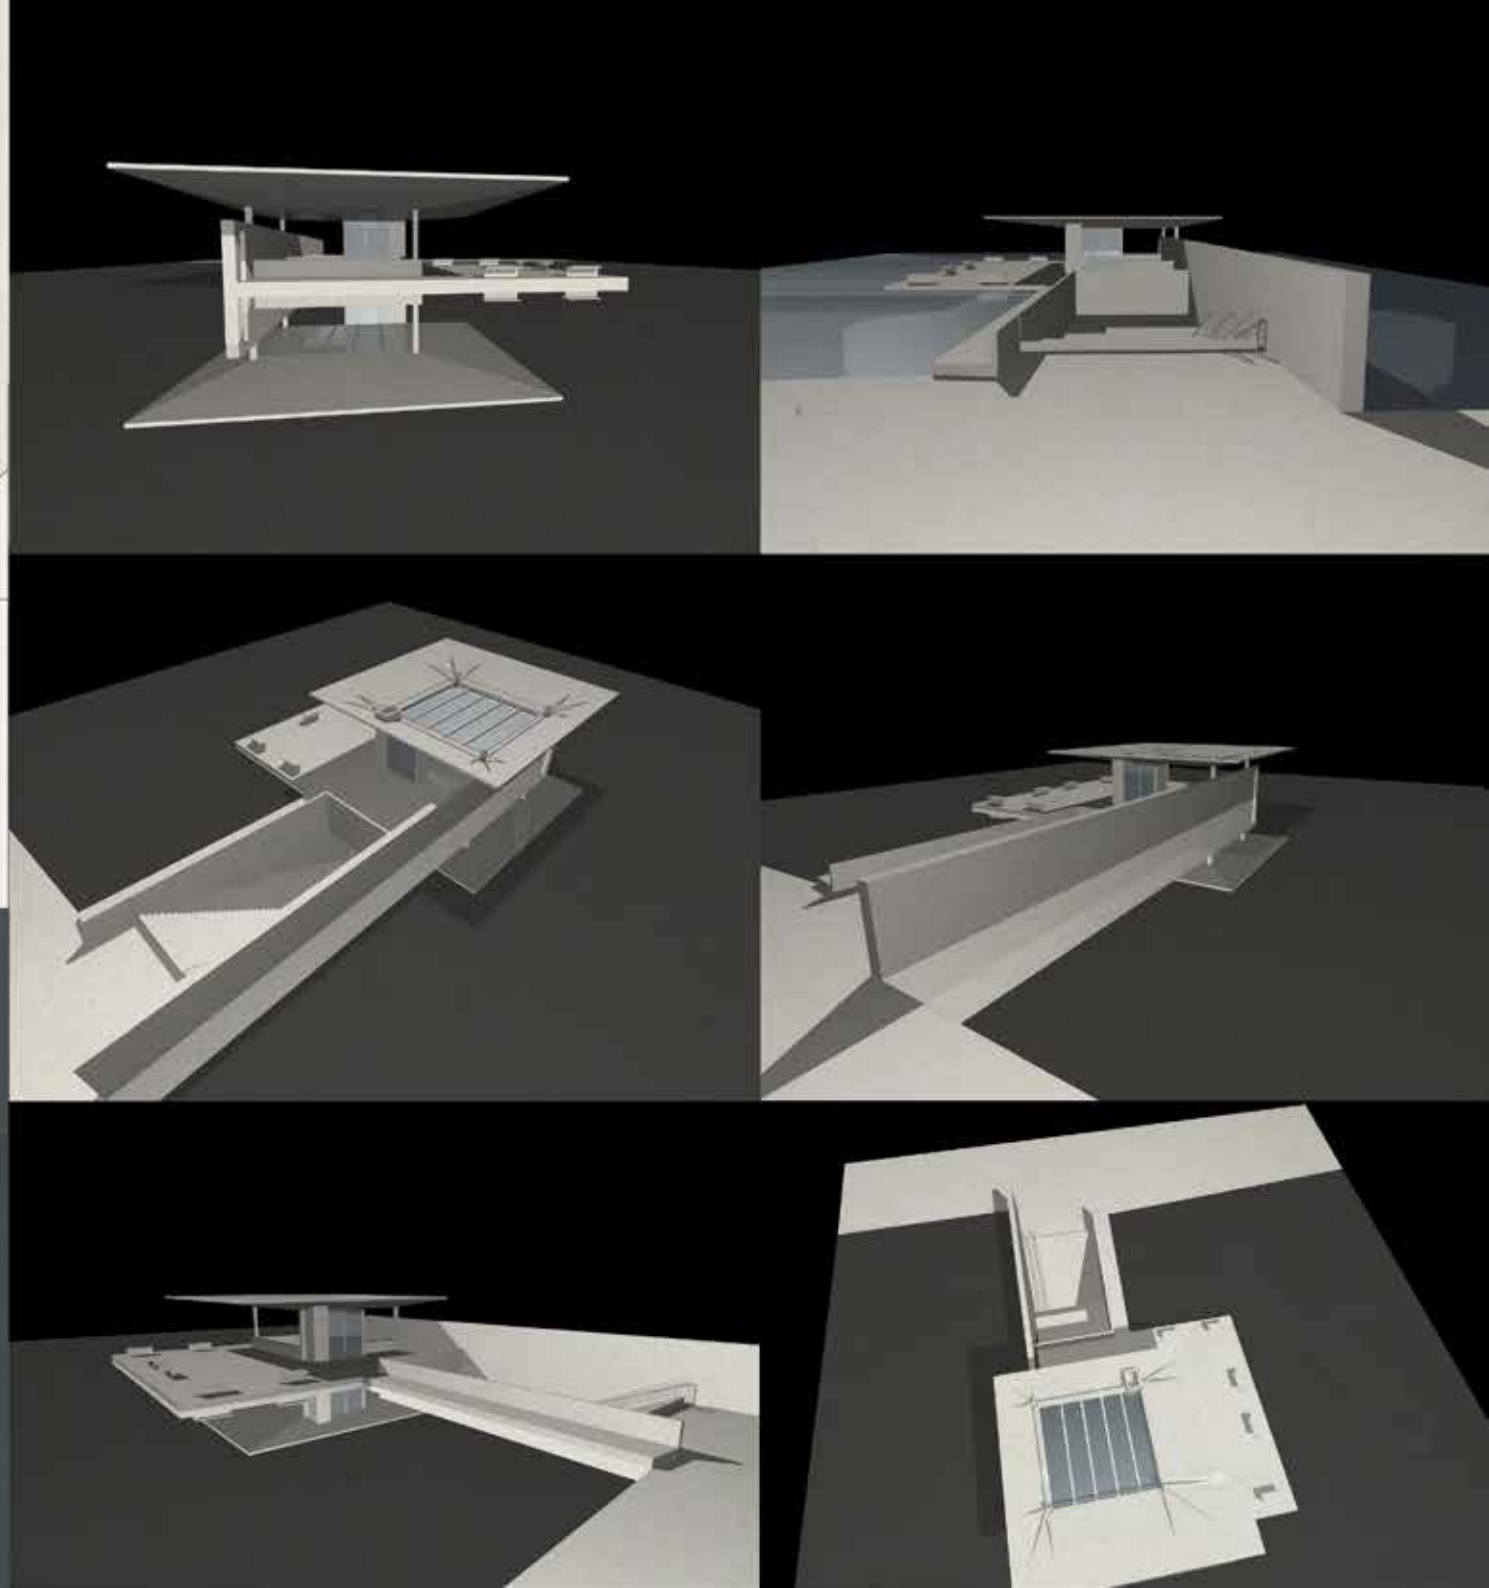

SUBWAY

VENICE_ZATTERE

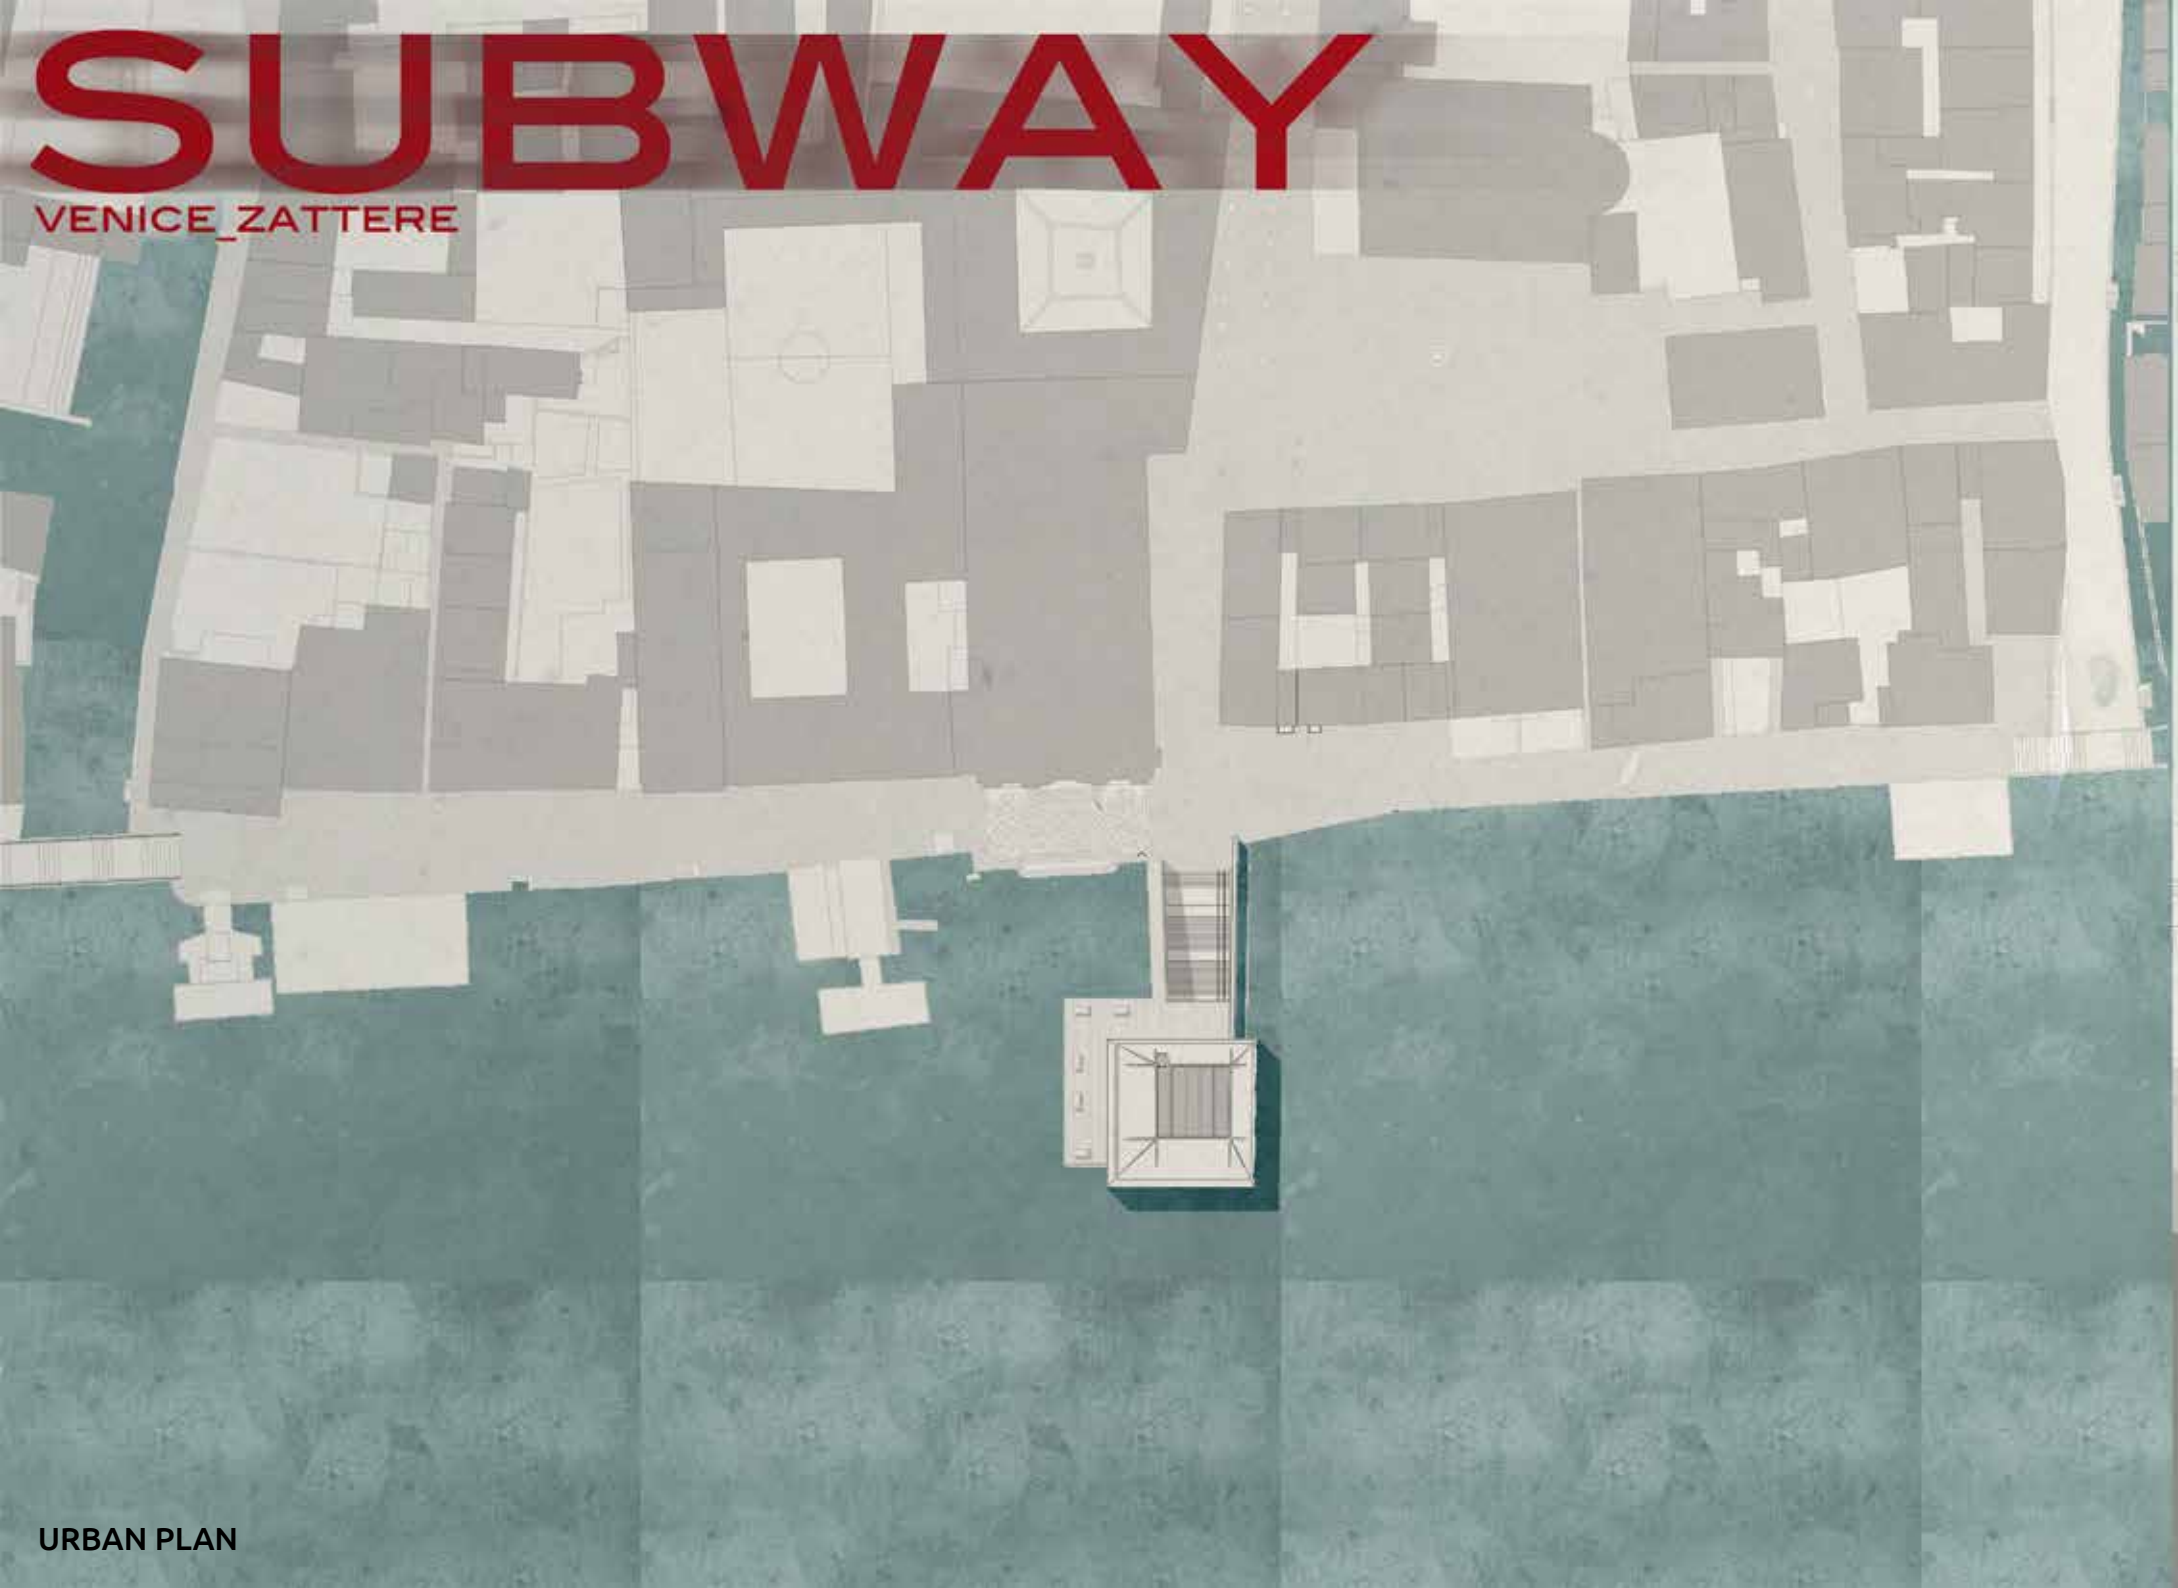

URBAN PLAN

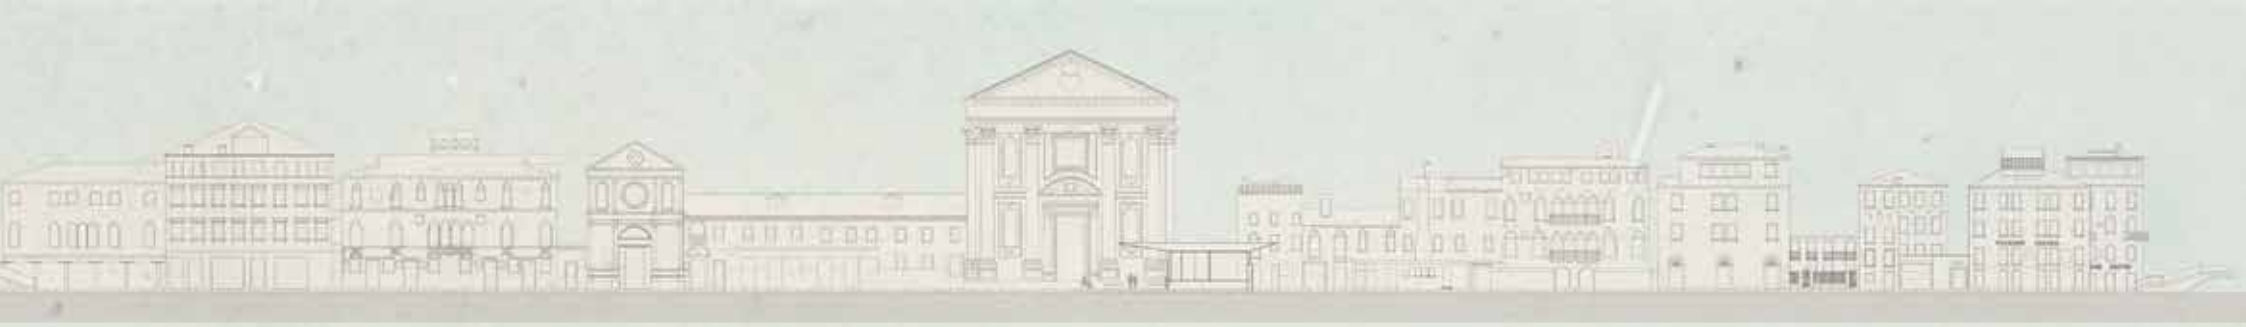

PROSPECT SUD

SECTION

SUBWAY

VENICE_ZATTERE

- building site, photo
- preliminary project for sub-lagoonar station
- maquette photos

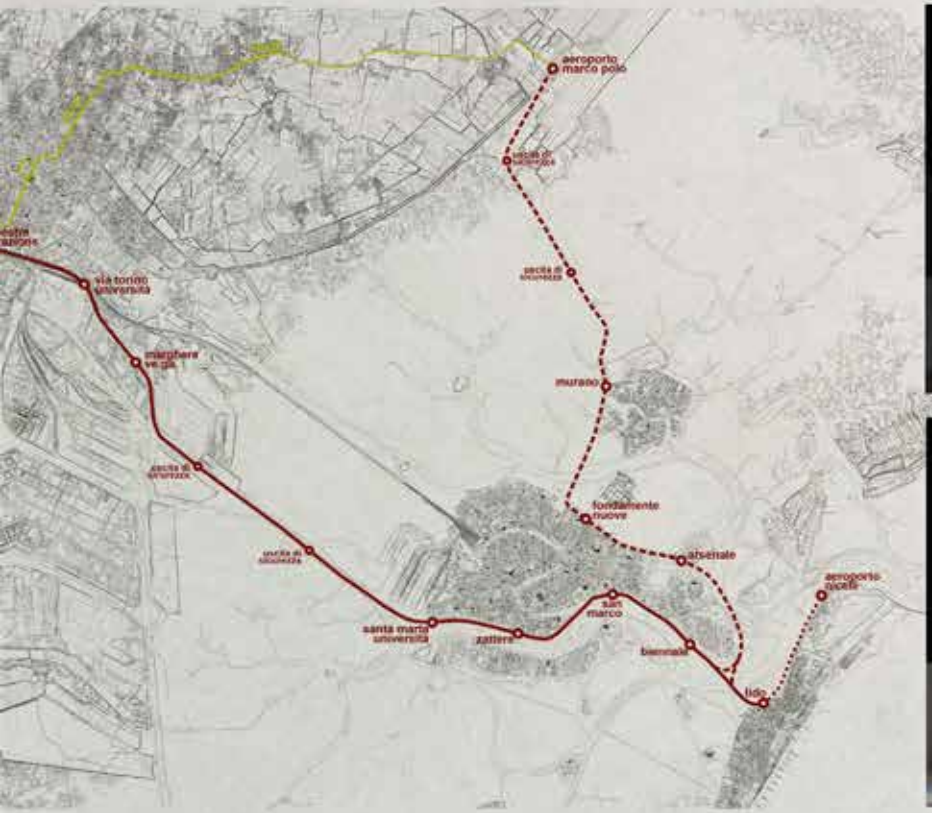

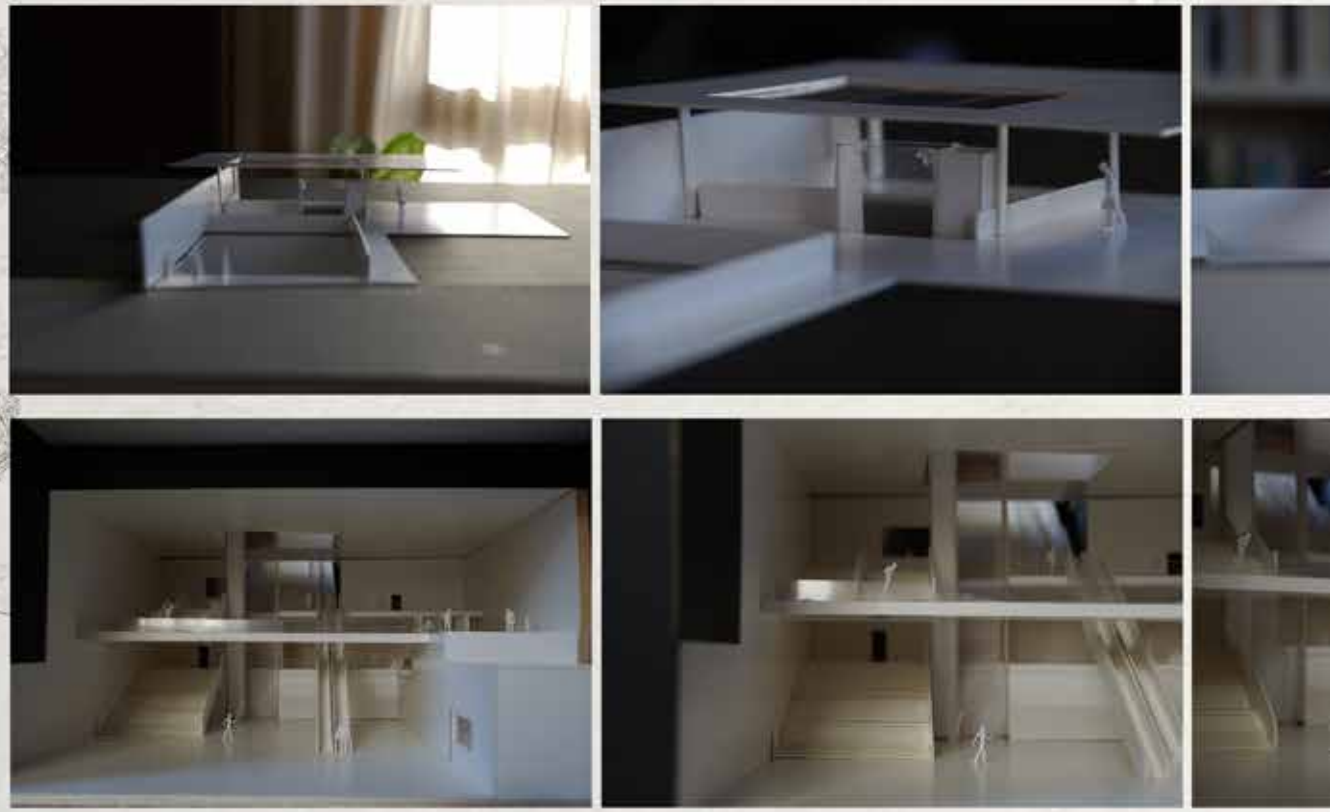

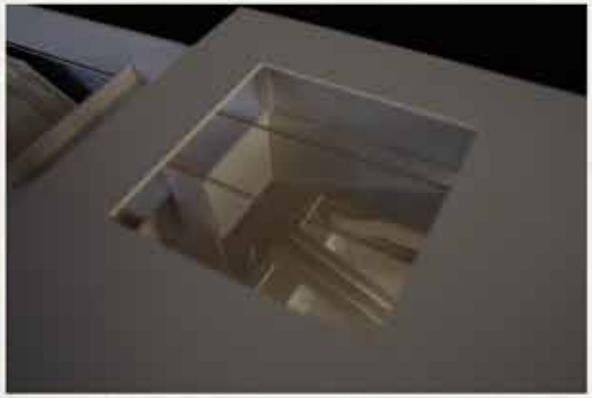

CONCORSI
COLLABORAZIONI
INTERESSI/FREELANCE

SEA TRACE IN A LIVING MARK
lighthouse sea hotel

An old lighthouse, a moon and bare setting.
Our aim is to bring those places back to life, taking into great consideration their inner characteristics.
Capo Muro di Porco represents an appealing and polyfunctional centre within an imaginary **maritime connection system**, which links several interesting places such as Catania and Pozzallo (Matta), the archeological park in Syracuse, the vineyard of Avola, Marzamemi and Pachino and the streams' island of Portopalo di Capopassero.
In order to emphasize the importance of the connection between the sea and the coasts, it has been decided to artificially reproduce this **relationship**.

This is the reason why, according to our project, the main entry to the lighthouse area comes from the sea: a promenade divided into various levels which follows the reef up to the lighthouse, offering an amazing view of the roundabouts and of the lighthouse itself.
From a planimetric point of view, the project is characterized by **two dominant elements linked by** a walk through: the existing lighthouse on one side and the new volume on the other.
From a functional point of view, the stair represents the connection point among the diverse activities that can be done. For instance information point, Hotel's hall and reception, the path to the rooms and finally a laboratory for marine biologist at sea level.
To avoid jeopardising of the non-manmade landscape, it has been privileged the reef as building site. Therefore, the hotel frameworks are built on the reef as if they are anchored to it, granting a breathtaking view on the sea.
The houses/snails, as parasite grabbed on the rocks, follow an ascendant path along the coasts' orography up to the hinterland pathways. Their location depends on environmental factors such as sun exposure. Indeed, they are built on the eastern area of the project where they are protected from the reef giving them shades during the day.
Pathways have been developed through the hinterland as well, so as to connect the lighthouse with various rest areas located in the southern part of the project, the most exposed to the sun.

This project is aimed also at creating cultural spaces by using existing factory sites nearby the lighthouse.
The proposal is to use these buildings to set up museums showing marine artifacts and wreck typical of the Pfemmiro area history.

In conclusion, the project has stared by considering the urban scale of the whole area nearby the Plemmiro peninsula, inserted within a broader aim of enhancing the seacoasts; as a consequence the main building element represents the connecting element between maritime paths and peninsula hinterland.
In particular it has been decided to **preserve the inner characteristics of the area** and the environmental integrity. Therefore, the building sites develop along the reef avoiding the exploitation of the maritime sanctuary.

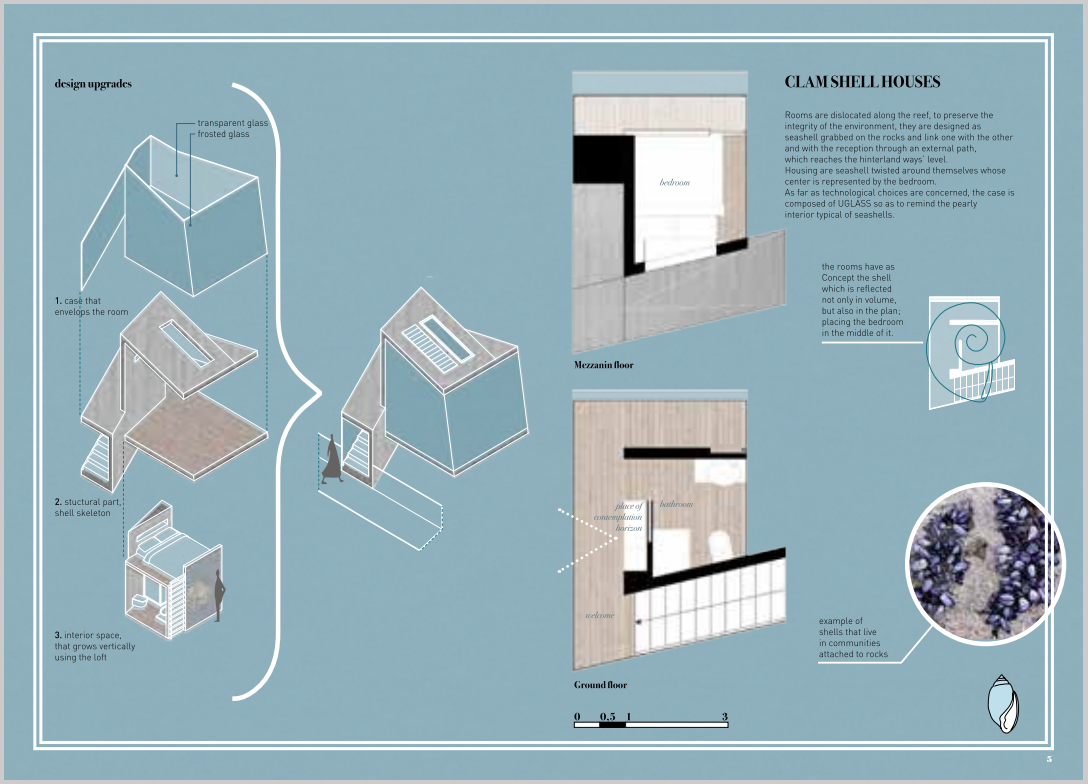

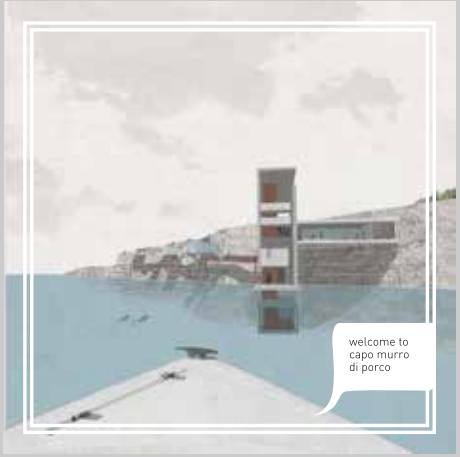

Learning room

1

6

CONCORSI
COLLABORAZIONI
INTERESSI/FREELANCE

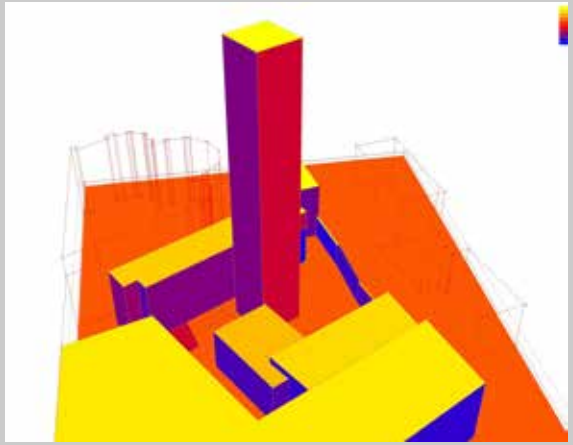

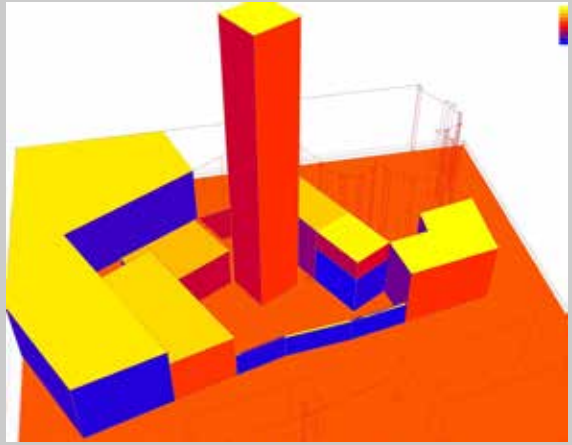

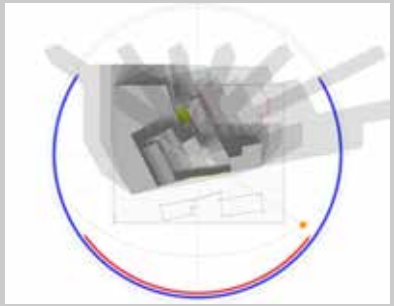

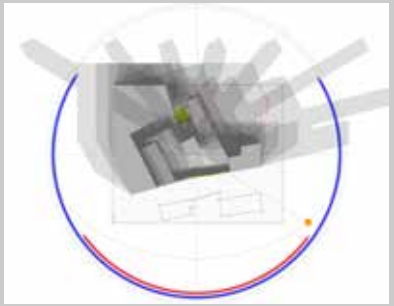

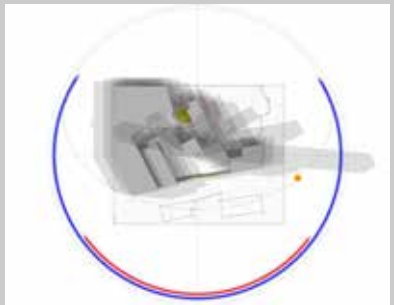

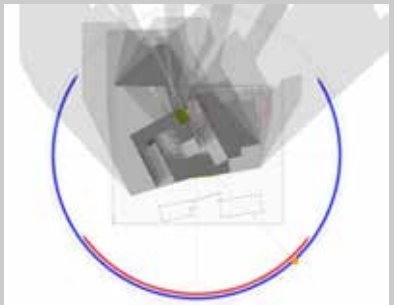

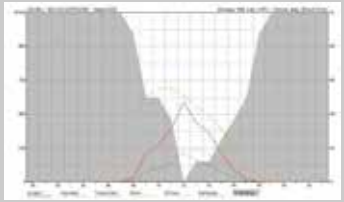

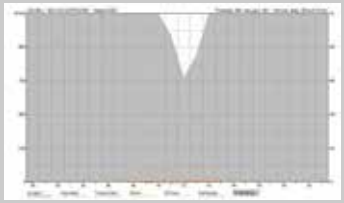

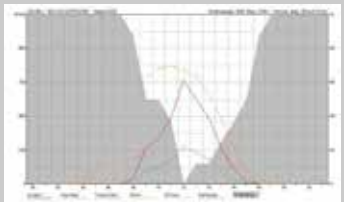

L'ORTO DEL CAMPANILE

Solar and climatic analysis for a correct disposition of plants inside the social vegetable garden behind the church of Santa Maria dei Carmini in Venice.
The project entailed the restoration of this spaces and return them back to the community.
The structure is now proudly open to the public after years of abandonement.
This urban garden was developed as social experiment and is now a good pole of attraction for the surrounding society.

CONCORSI
COLLABORAZIONI
INTERESSI/FREELANCE

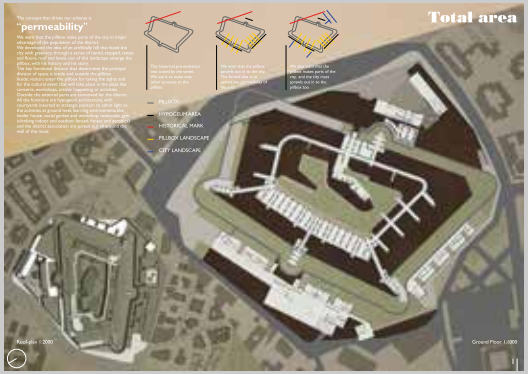

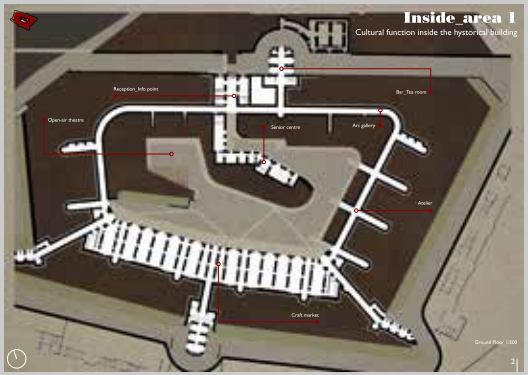

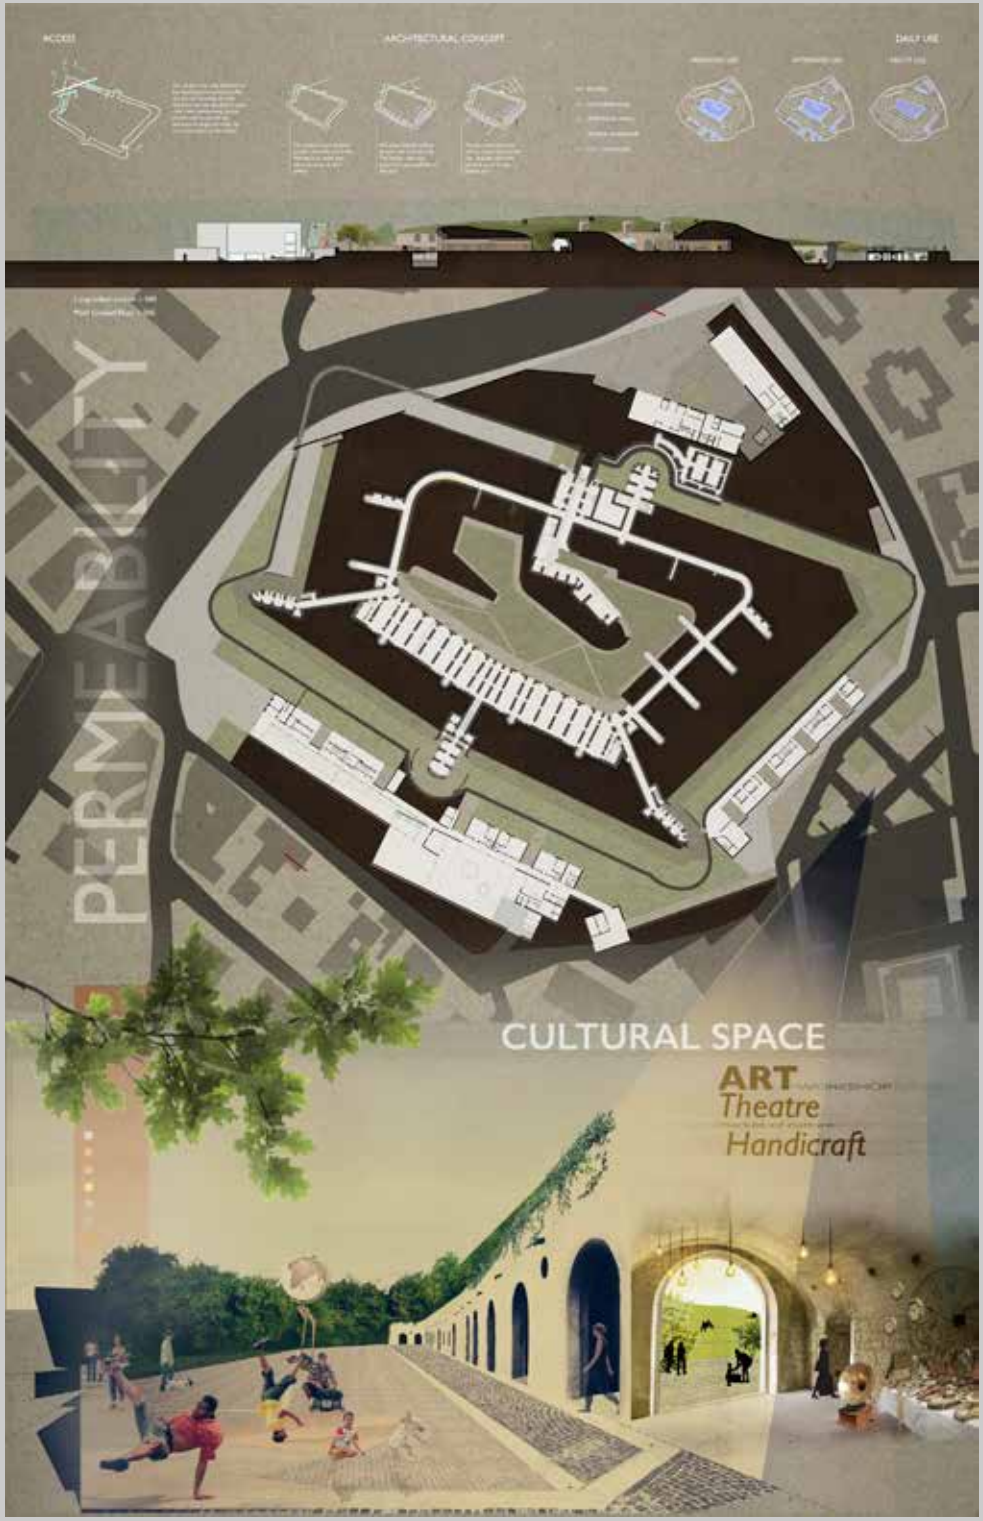

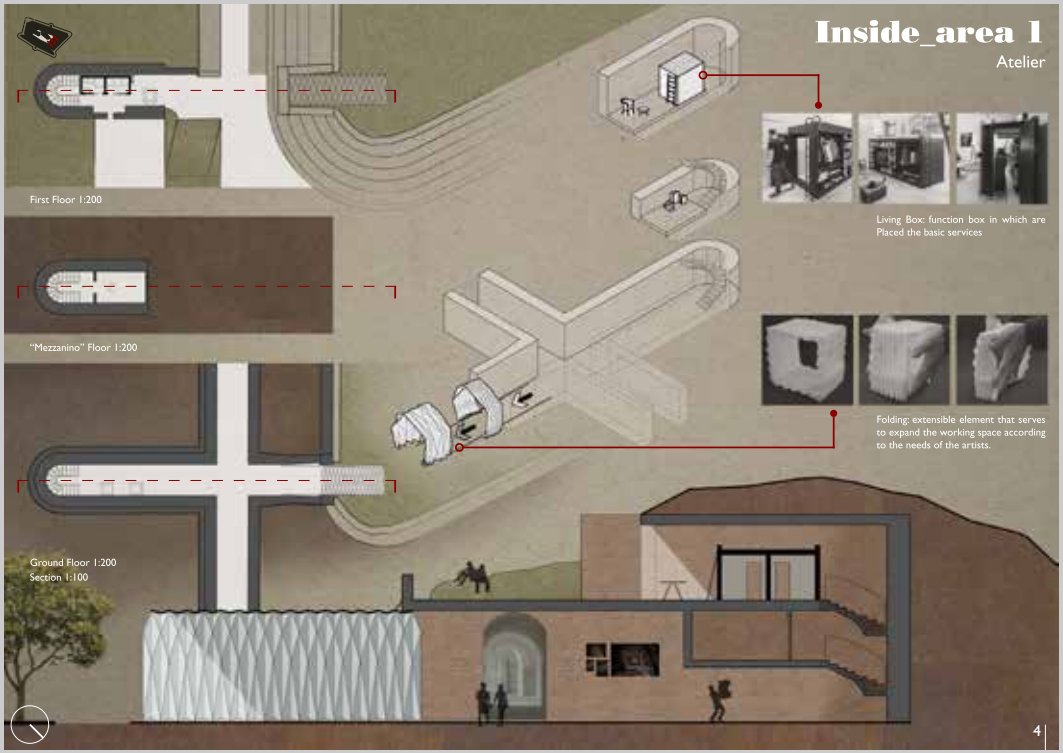
Inside_area 1
Atelier
First Floor 1:200
"Mezzanino" Floor 1:200
Ground Floor 1:200
Section 1:100
Living Box: function box in which are Placed the basic services
Folding: extensible element that serves to expand the working space according to the needs of the artists.
4

Outside_area 2
Kindergarten_Learning environments
Section 1:200
Kindergarten
Learning environments
Ground Floor 1:500
7

Inside_area 1
Senior centre_Craft market
Lutist
Potter
Bricolage
Blacksmith
Carpenter
Tailor
Cobbler
ART & CRAFTS
Inside Area Program function
Access and permeability of the inside areas of the Forte.
Intside Area Daily use
Morning use
Afternoon use
Night use
Atelier
Bar / Tea room
Senior centre
Craft market
Open-air theatre
Section 1:200
3

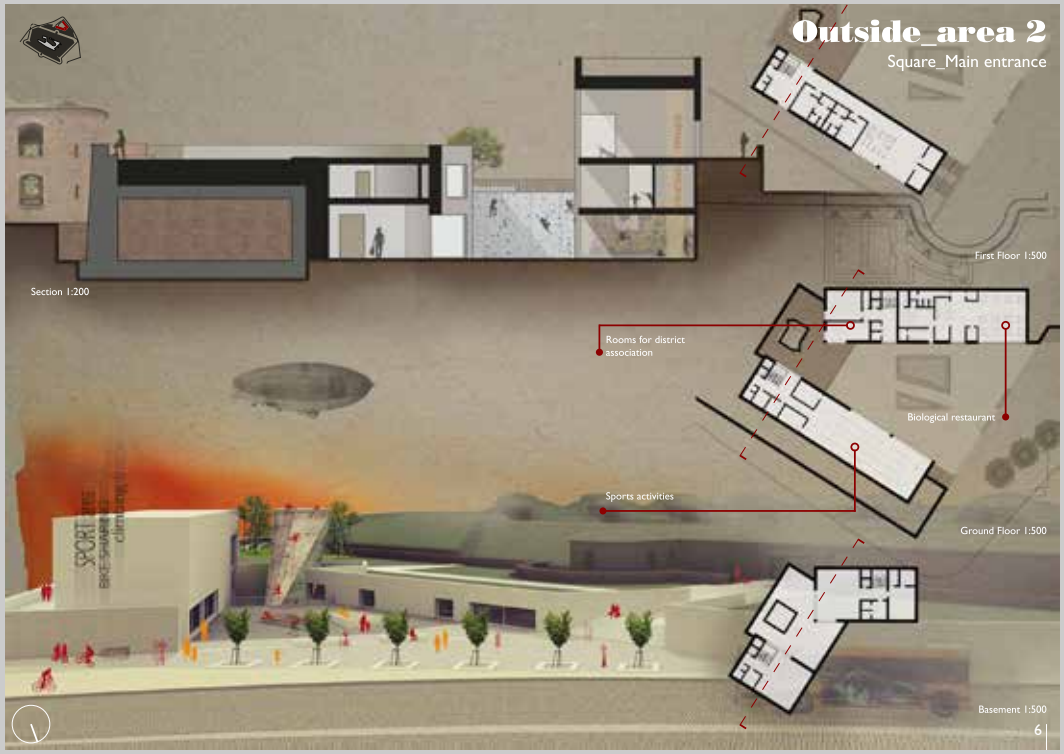
Outside_area 2
Square_Main entrance
Section 1:200
First Floor 1:500
Rooms for district association
Biological restaurant
Sports activities
Ground Floor 1:500
Basement 1:500
6

CONCORSI
COLLABORAZIONI
INTERESSI/FREELANCE

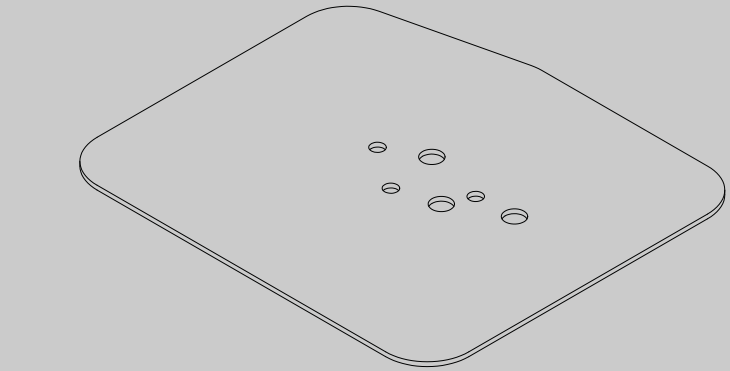

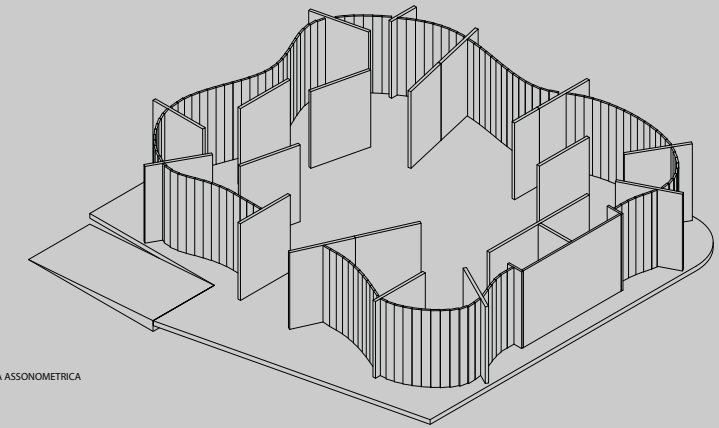

VISTA ASSONOMETRICA

ECOFONDACO SENSORIALE
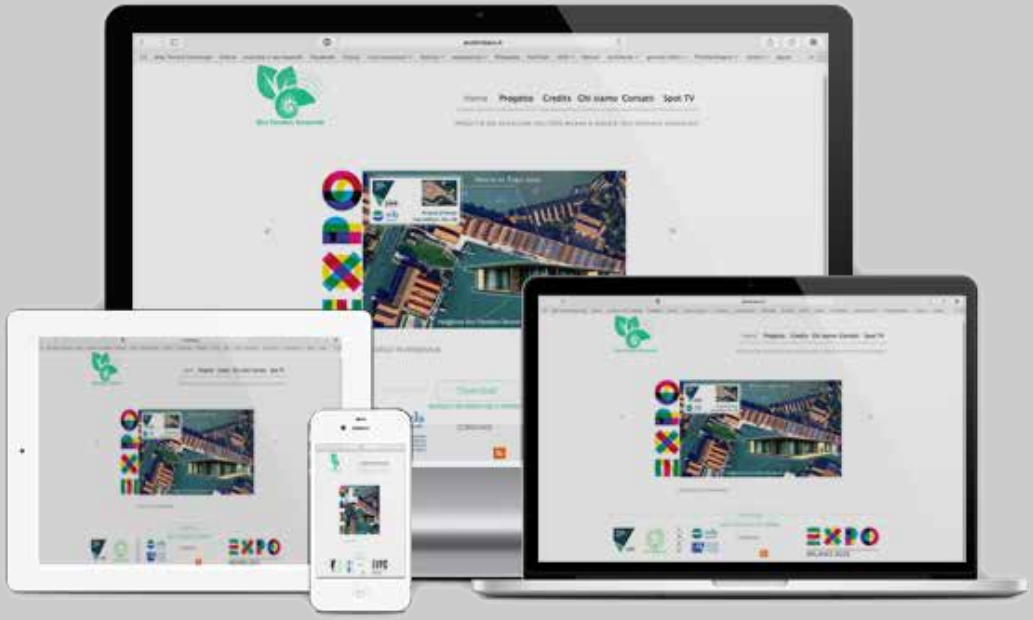
The Pavillion was proposed for Expo 2015, Venice was the only sister city for the international exposizion in Milan. Green Communication agency elaborate the project in collaboration with IUAV.